
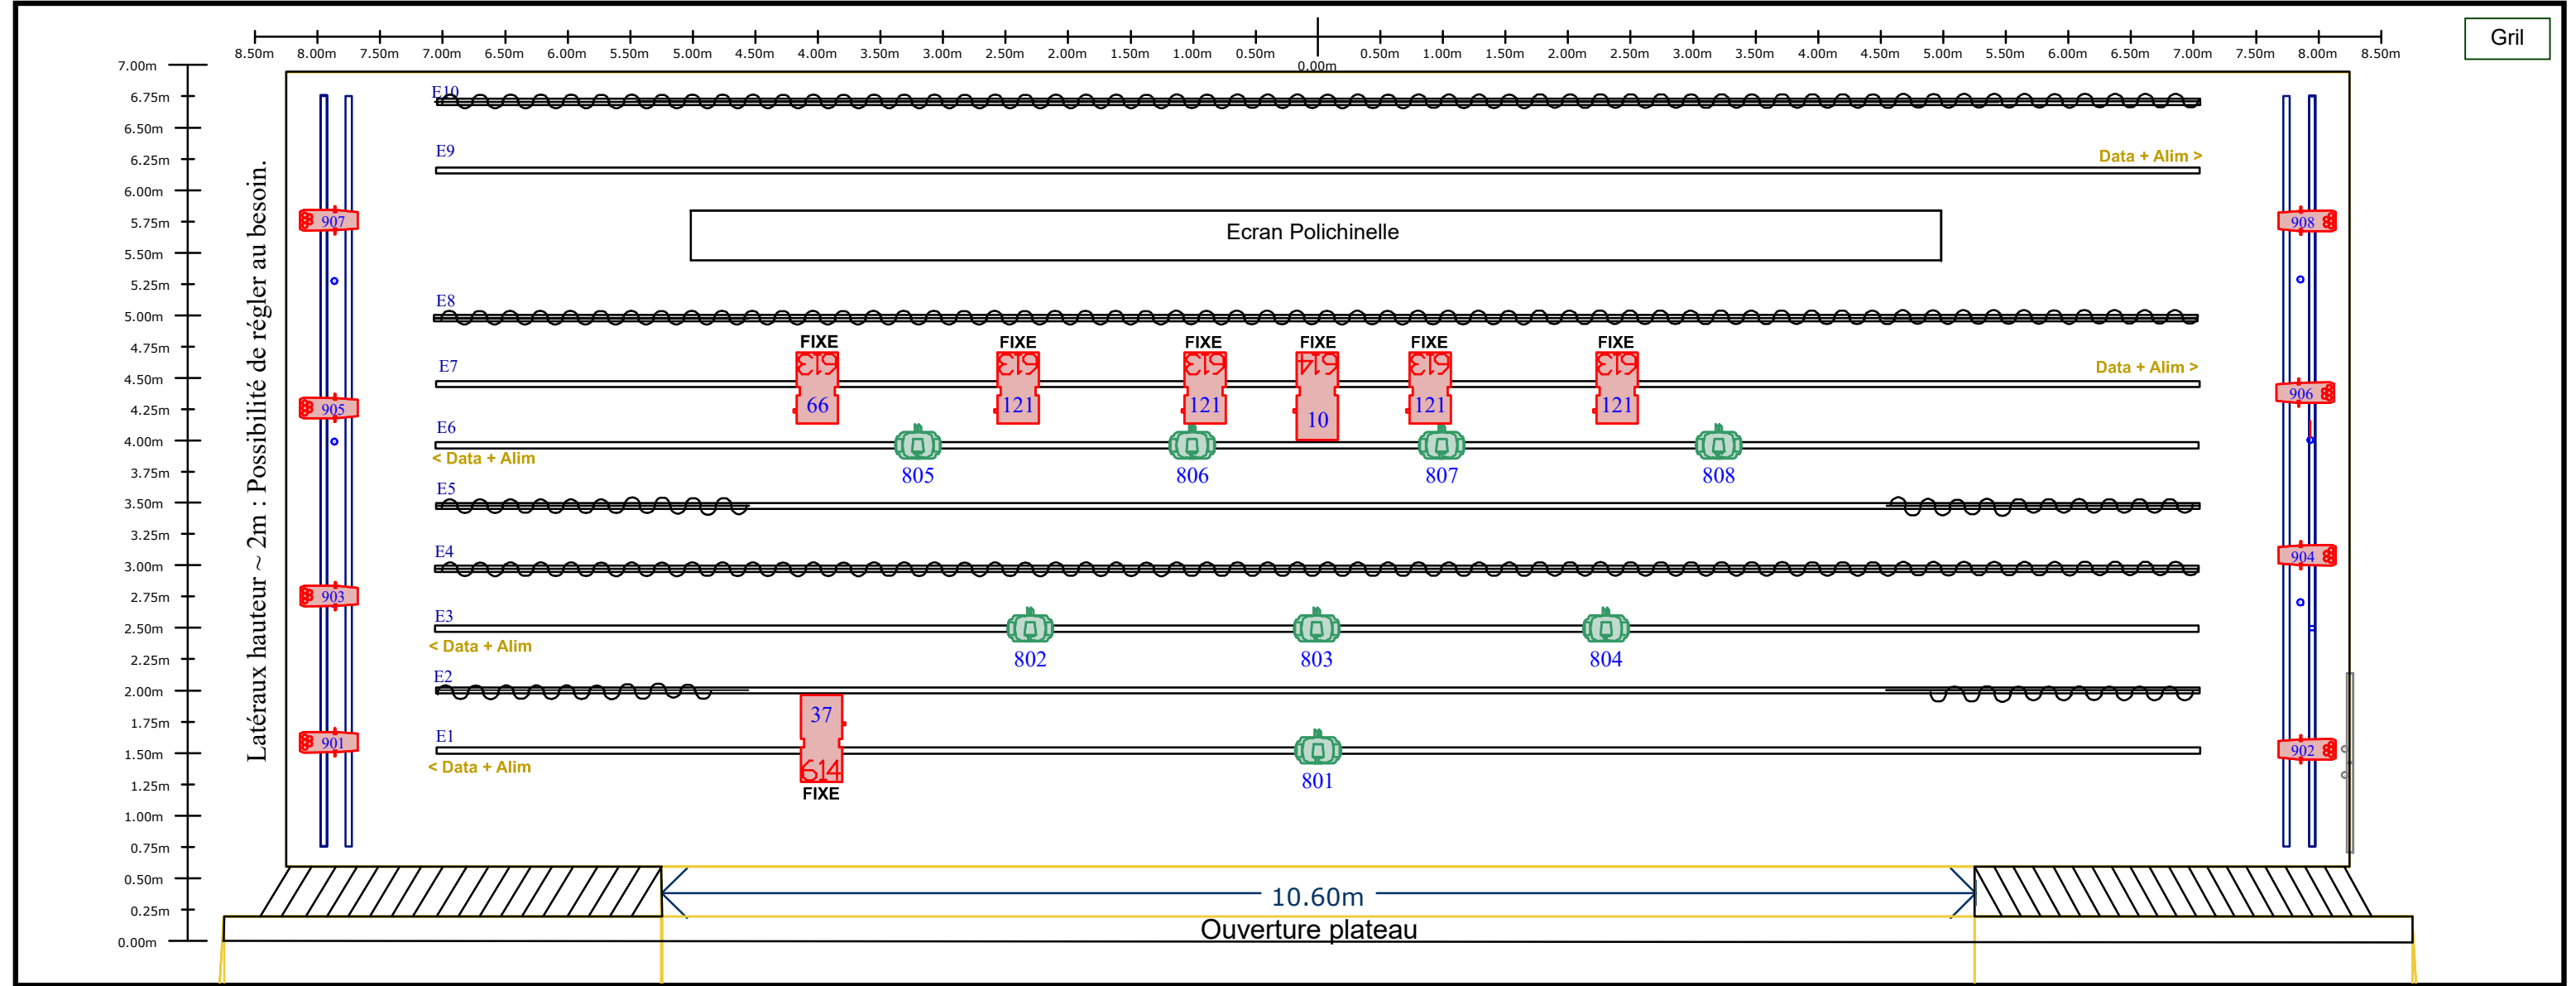
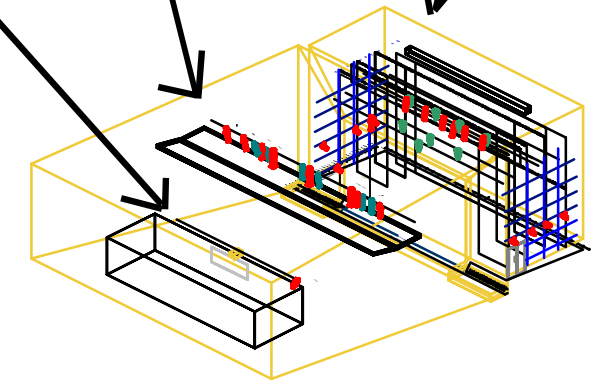


Symbole	Nom	Compte
	RJ 614SX 1kw (équipé de trappe SULLY LED 115w 3000K)	7
	RJ 613SX 1kw (équipé de trappe SULLY LED 115w 3000K)	4
	RVE TwinLed 75w	6
	Par 64	12
	Robert Juliat PC 1kw	8
	Ayrton Diablo TC	8
	Ayrton Mistral TC	8
	Ayrton NandoBeam S6	6
	ColorSun 200S	4
	Showtec Octostrip 1m	16
	Sunstrip Active Dmx	12
	Blinder Chauvet Shocker P2	6

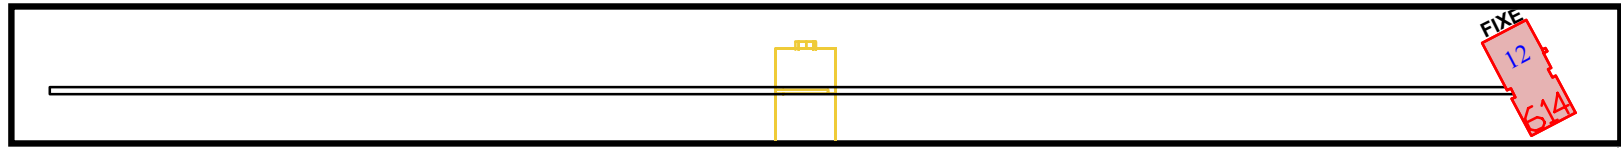

Plan de Feu 2025/2026 - Auditorium

Les projecteurs en rouge mentionnés "FIXE" ne seront ni déréglés, ni déplacés.